

Jabatan Operasi Sistem



Substation: **ARA DAMANSARA**

Mnemonic: **ADAM**

Voltage: **132kV**

Drawing No.: **1-CYA-ADAM-1446**

Date Drawn: **16th. APR., 2013**

Date Updated: **21th. AUG., 2018**

Rev: **2/17**

Area: **KUALA LUMPUR**


PLC: **-**

Tel: **-**

Drawn by: **ARJURIN**

Checked by: **HAFIZAN**

Approved by: **AZMI/Ir.FAROUK**

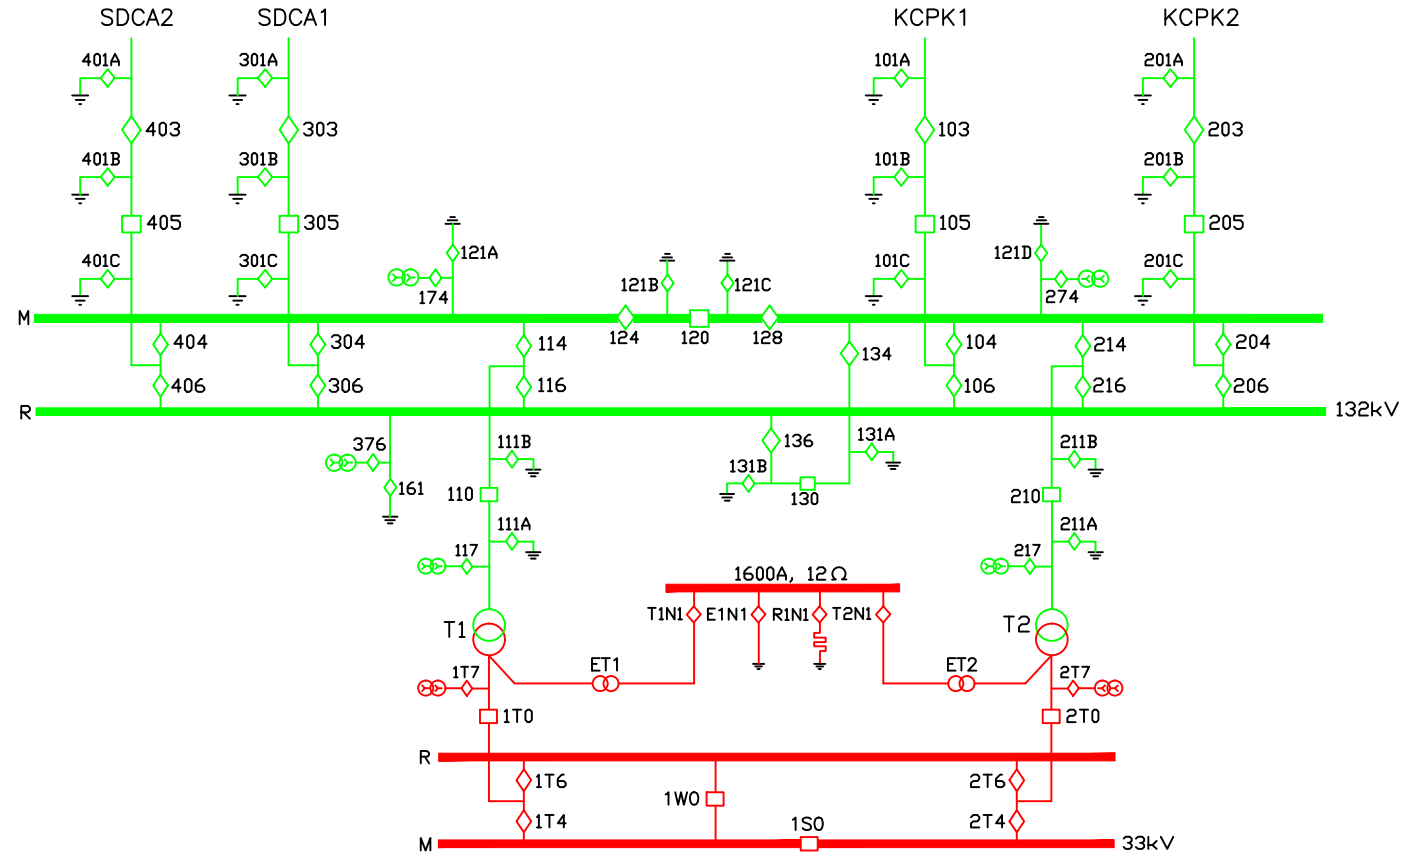

Transformer Rating

132/33 kV **2x90 MVA** Total Cap.: **180** Vector Group: **Yd1**

Commissioning Date

T1 21/8/17

T2 21/8/17

REMARKS:

1/17-Substation was comm. on 12/8/17.
2/17-Feeder to SDCA1 & KCPK1 was comm. on 19/8/17.
-T1 & T2 was comm. on 21/8/17.

1-CYA-ADAM-1446